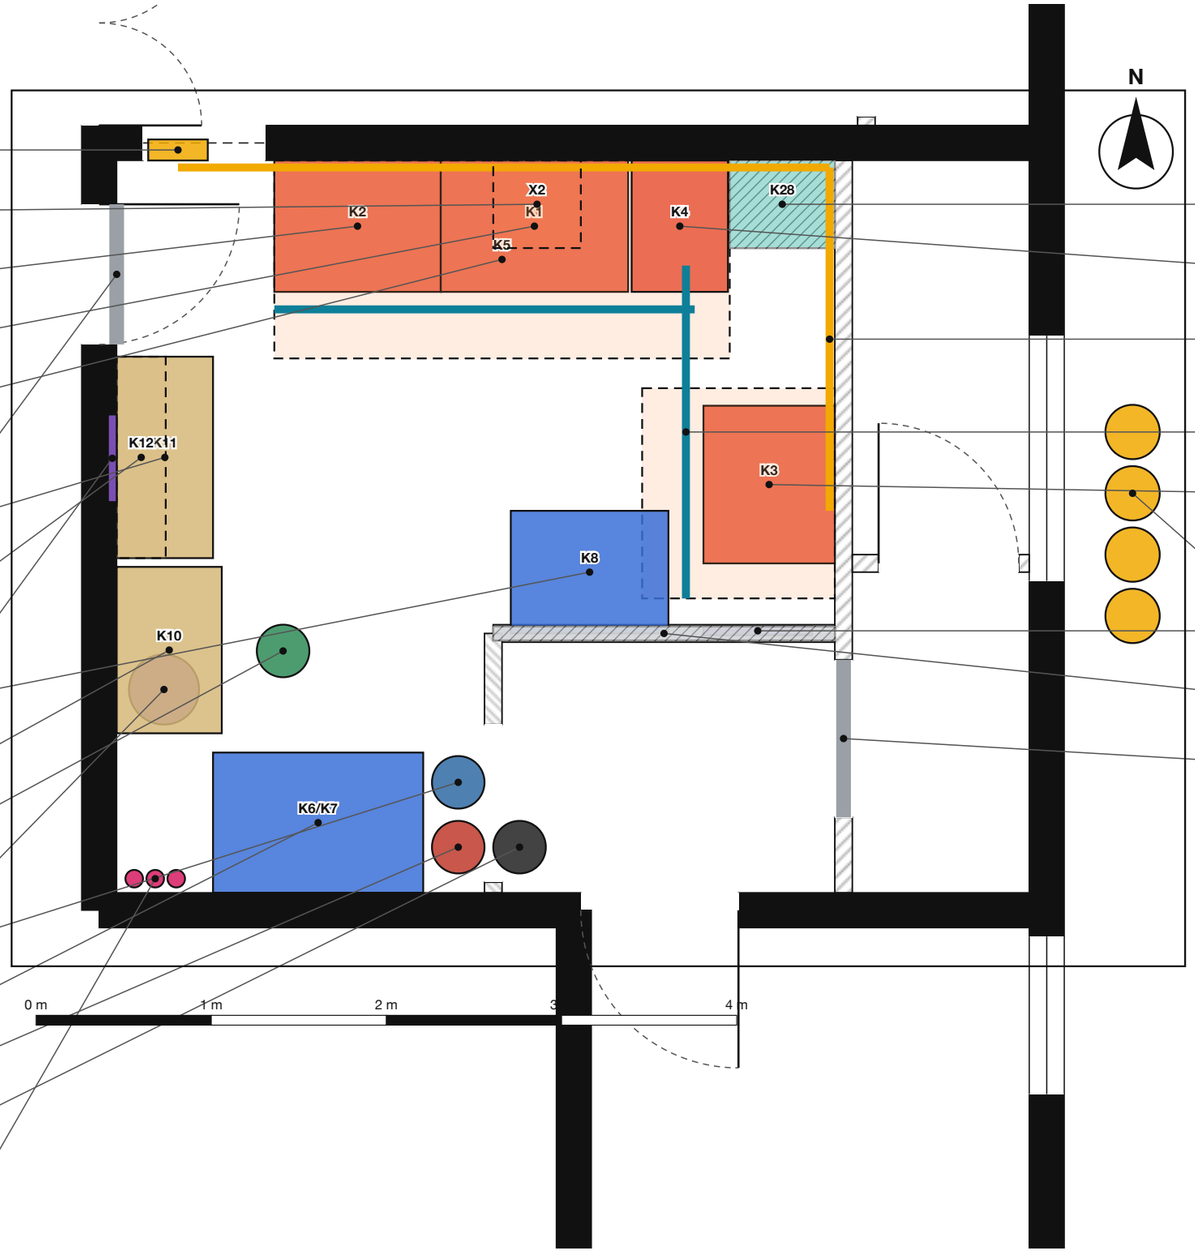


K29 Gas shut-off + detector
0.30 × 0.12 × 0.30

X2 Duct from the hood, across the dish wash
0.50 × 2.00 × 0.40

K2 Stock / pot range, 2 burners
0.95 × 0.75 × 0.80

K1 Wok range, 2 burners
1.07 × 0.75 × 0.85

K5 Exhaust hood
2.60 × 1.13 × 0.50

K30 Kitchen door 0.80 m, steel, self-closing
0.80 × 0.05 × 2.05

K11 Pass table, by the door
0.55 × 1.15 × 0.92

K12 Wall shelf, one tier
0.30 × 1.15 × 0.04

K27 KDS screen S2, 21.5 in
0.50 × 0.05 × 0.29

K8 Under-counter chiller + raw bench
0.90 × 0.70 × 0.90

K10 Veg prep bench
0.60 × 0.95 × 0.90

K19d Dustbin, green: veg waste (under K10)
0.35 × 0.35 × 0.55

K14 Rice cooker, 10 L
0.45 × 0.45 × 0.45

K19c Dustbin, blue: recycling
0.35 × 0.35 × 0.55

K6/K7 Dual-zone upright: chiller + freezer
1.20 × 0.80 × 1.95

K19a Dustbin, red: non-veg waste
0.35 × 0.35 × 0.55

K19b Dustbin, black: dry waste
0.35 × 0.35 × 0.55

K20 Fire extinguishers ×3 and fire blanket
0.15 × 0.15 × 0.50 each

K28 Sink (existing, NE corner) (existing)
0.60 × 0.50 × 0.85

K4 Dim sum steamer, 1 station
0.55 × 0.75 × 0.90

K29p Gas pipe (brass) along the north and east walls at 1.0 m, branching to every burner
about 6.5 m run

Y1 Hot-line floor trough (drain), L-shaped
4.30 × 0.10 × 0.10

K3 Twin-tank fryer, 2 × 15 L
0.90 × 0.75 × 0.90

LPG bank of 4 × 19 kg gas cylinders, outside the east wall (position to confirm)
0.31 Ø × 0.80 each

K26 KDS screen S1, 27 in
0.62 × 0.05 × 0.37

K31 False partition (existing) (existing)
1.95 × 0.10 × 2.20

K32 Washroom opening in the temporary wall (existing)
0.90 × 0.10 × 2.05

- Gas: cooking appliances
- Gas: pipe, shut-off valve, cylinders
- Refrigeration (chillers, freezers)
- Water: sinks, tank, heater, drain grating
- Tables, benches, shelves, racks and cabinets
- Dustbins (own colour)
- Electrics: screens, POS, small appliances
- Safety: extinguishers
- Exhaust hood and duct (overhead)
- Floor drain trough
- Structure and openings: doors, hatch, partition, pillar


PROJECT
Cabin East Garden, Goa · kitchen block, dish wash, bar, store room

DRAWING
Kitchen: colour-coded equipment
Every item by type, with its name and size (W × D × H, metres). Gas appliances red, gas pipe and cylinders amber, bins in their own colours

SCALE AT A3	SHEET	DATE	REVISION
1:35	**E-01**	3 Nov 2026	P1 draft

STATUS	BASIS
PRELIMINARY, for review	Client site sketches and photos; clear dimensions in metres

Not for construction. Sizes marked as assumed are not measured: confirm on site before ordering or building.

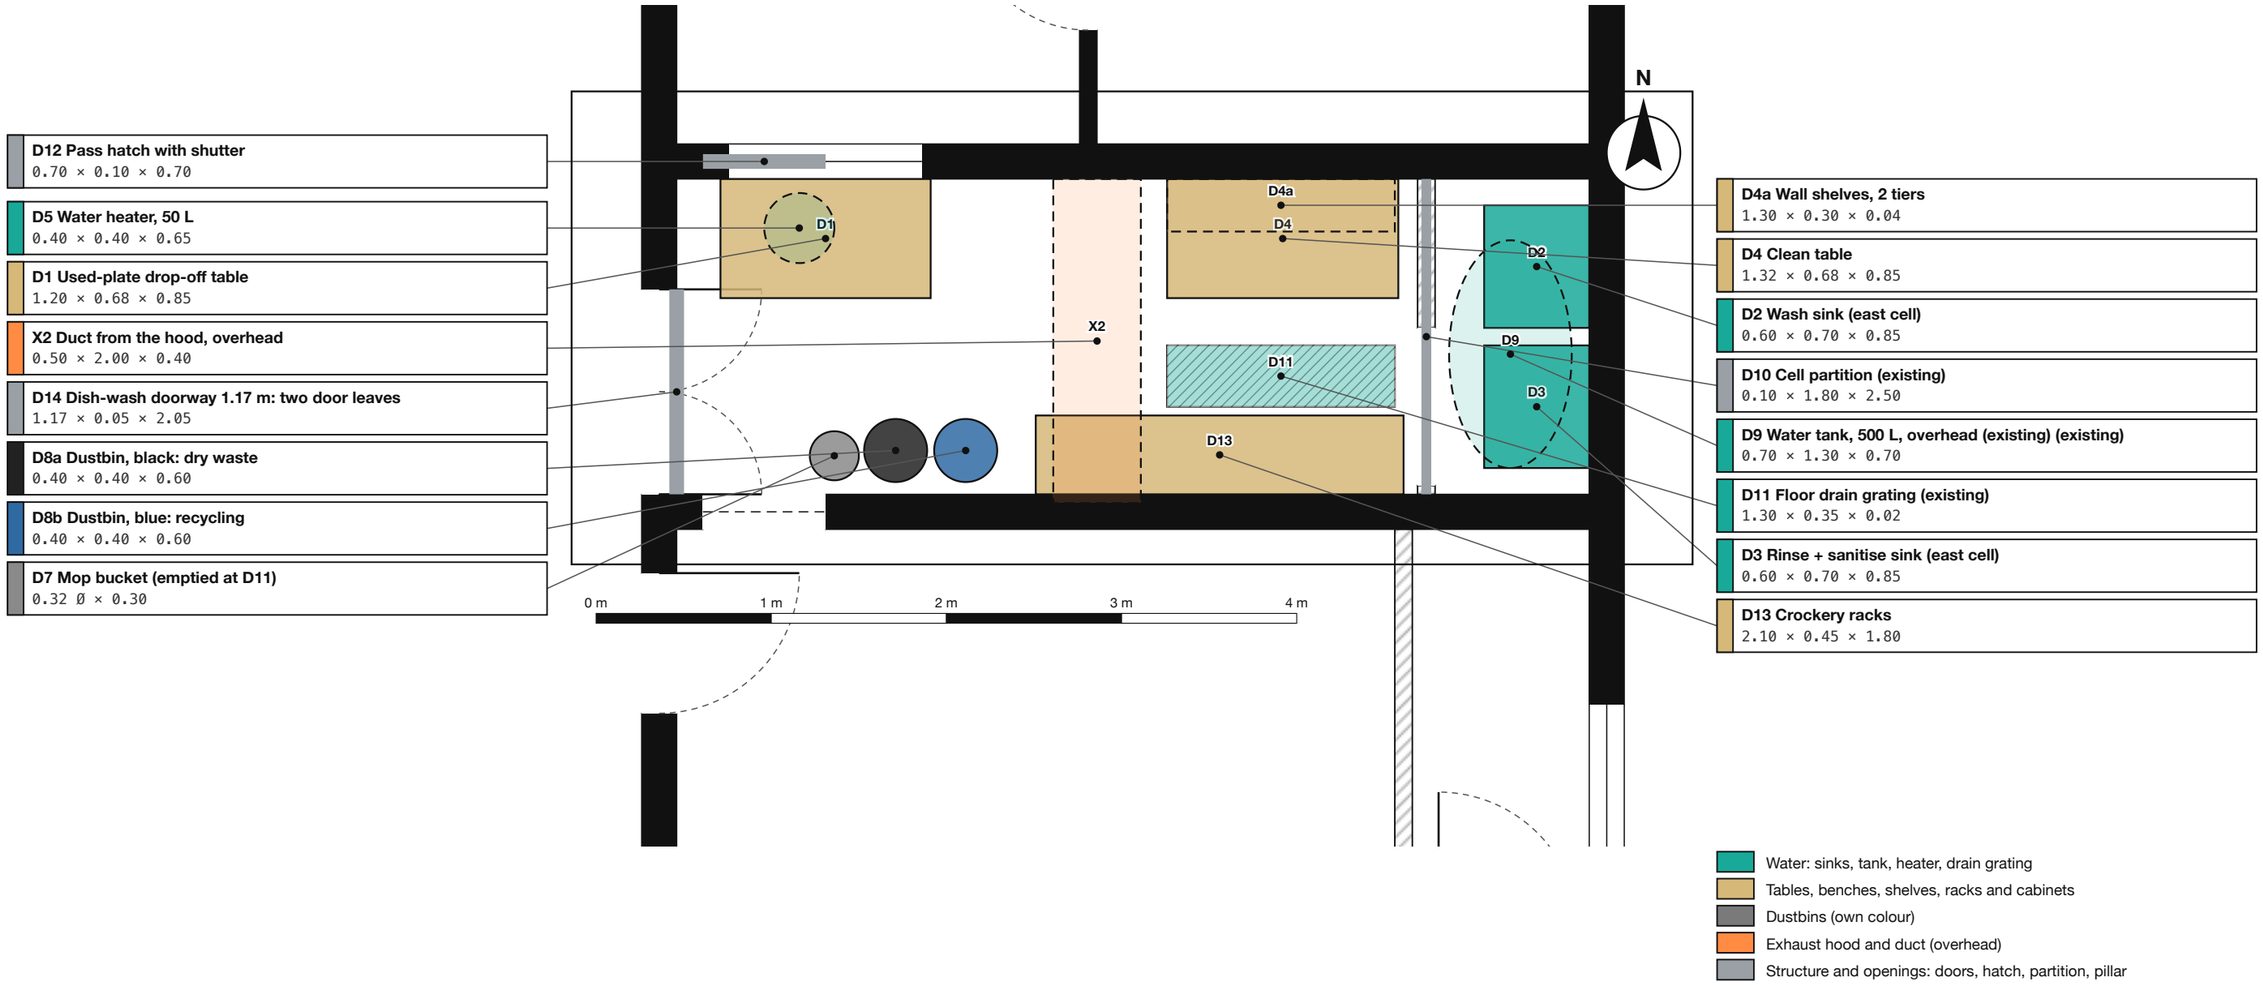


PROJECT
Cabin East Garden, Goa · kitchen block, dish wash, bar, store room

DRAWING
Dish wash: colour-coded equipment
Drop-off table, clean table, crockery racks, the two-sink cell with the 500 L tank above

SCALE AT A3	SHEET	DATE	REVISION
1:35	**E-02**	3 Nov 2026	P1 draft

STATUS	BASIS
PRELIMINARY, for review	Client site sketches and photos; clear dimensions in metres

Not for construction. Sizes marked as assumed are not measured: confirm on site before ordering or building.

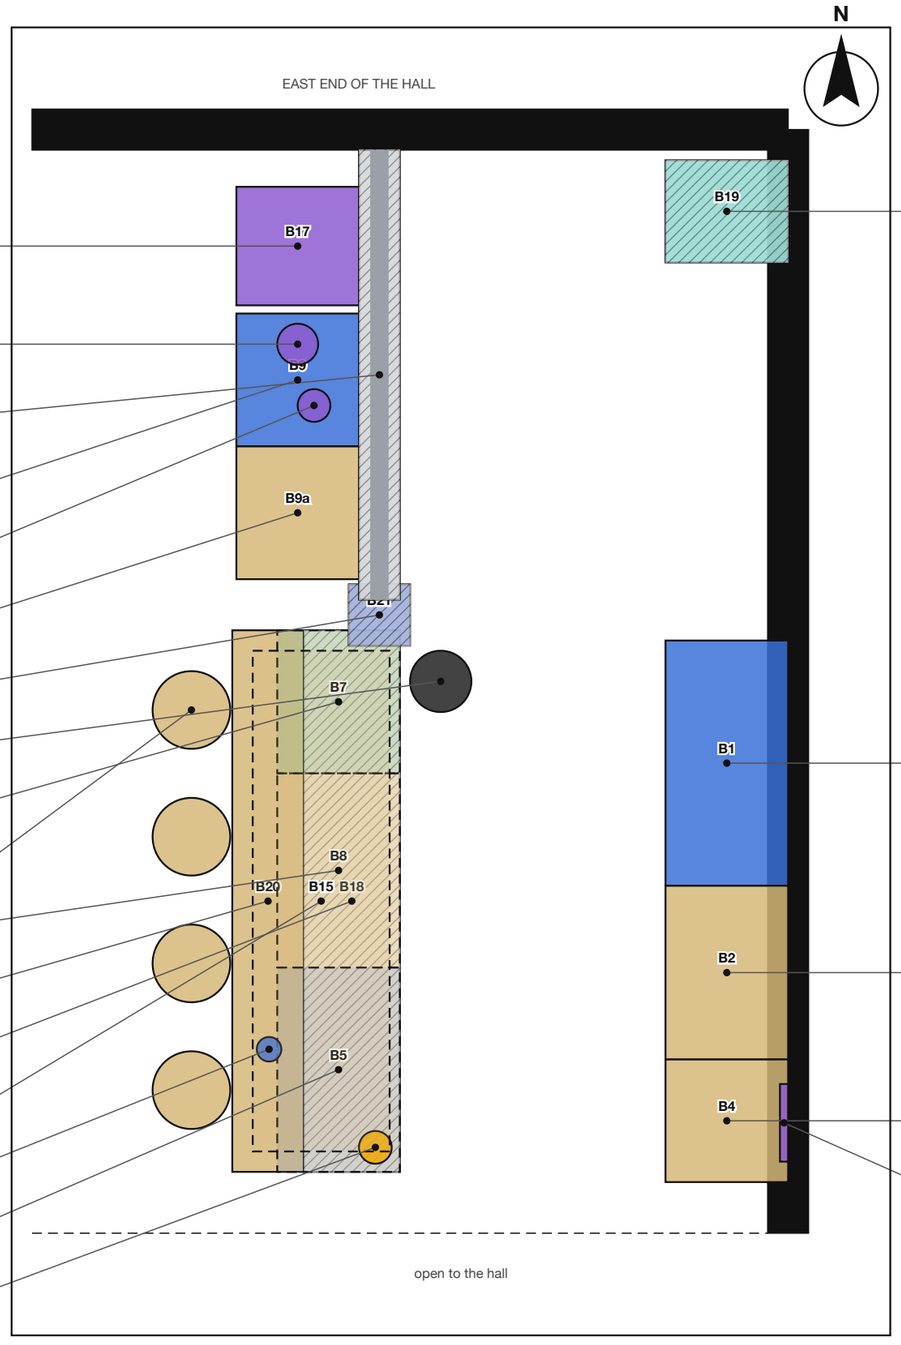

B17 POS desk
0.58 × 0.60 × 0.92

B11 Filter-coffee brewer
0.45 × 0.40 × 0.65

CW Coffee wall, brick, 2.20 m long (existing) (existing)
2.20 × 0.20 × full height

B9 Under-counter fridge
0.60 × 0.60 × 0.85

B12 Hot-water urn
0.30 × 0.30 × 0.55

B9a Cupboard under the coffee station (cups, filters)
0.60 × 0.60 × 0.85

B21 Blue pillar (existing) (existing)
0.30 × 0.30 × 3.00

B14 Bar bin, black: waste
0.30 × 0.30 × 0.50

B7 Sink with ice well
0.70 × 0.55 × 0.85

ST Bar stools ×4, seat 0.735 m
0.38 Ø × 0.75

B8 Lockable cabinet
0.95 × 0.60 × 0.85

B20 Bar top, 1.08 m high
2.65 × 0.35 × 1.08

B18 Wooden slab, 0.47 wide (existing) (existing)
2.65 × 0.47 × 0.92

B15 Hanging glass rack
2.60 × 0.67 × 0.28

B6 Tap font, 3 taps
0.60 × 0.20 × 0.45

B5 Keg chiller, 3 kegs
1.00 × 0.60 × 0.85

CO_2 Gas cylinder (CO_2) for the kegs, 2–3 kg, chained beside the keg chiller
0.15 Ø × 0.50

B19 Sink in the aisle (existing) (existing)
0.60 × 0.50 × 0.85

B1 Bottle cooler, 2 glass doors
1.20 × 0.60 × 0.85

B2 Base cabinet (plain)
0.85 × 0.60 × 0.85

B4 Back-bar cabinet
0.60 × 0.60 × 0.85

B16 KDS screen S3, 15.6 in
0.38 × 0.03 × 0.23

0 m 1 m 2 m 3 m 4 m

- Refrigeration (chillers, freezers)
- Water: sinks, tank, heater, drain grating
- Tables, benches, shelves, racks and cabinets
- Electrics: screens, POS, small appliances
- Gas: pipe, shut-off valve, cylinders
- Dustbins (own colour)
- Structure and openings: doors, hatch, partition, pillar

PROJECT
Cabin East Garden, Goa · kitchen block, dish wash, bar, store room

DRAWING
Bar: colour-coded equipment
Counter with the raised bar top over the work slab, coffee station on the coffee wall, keg chiller and its CO_2 cylinder

SCALE AT A3	SHEET	DATE	REVISION
1:30	**E-03**	3 Nov 2026	P1 draft

STATUS	BASIS
PRELIMINARY, for review	Client site sketches and photos; clear dimensions in metres

Not for construction. Sizes marked as assumed are not measured: confirm on site before ordering or building.