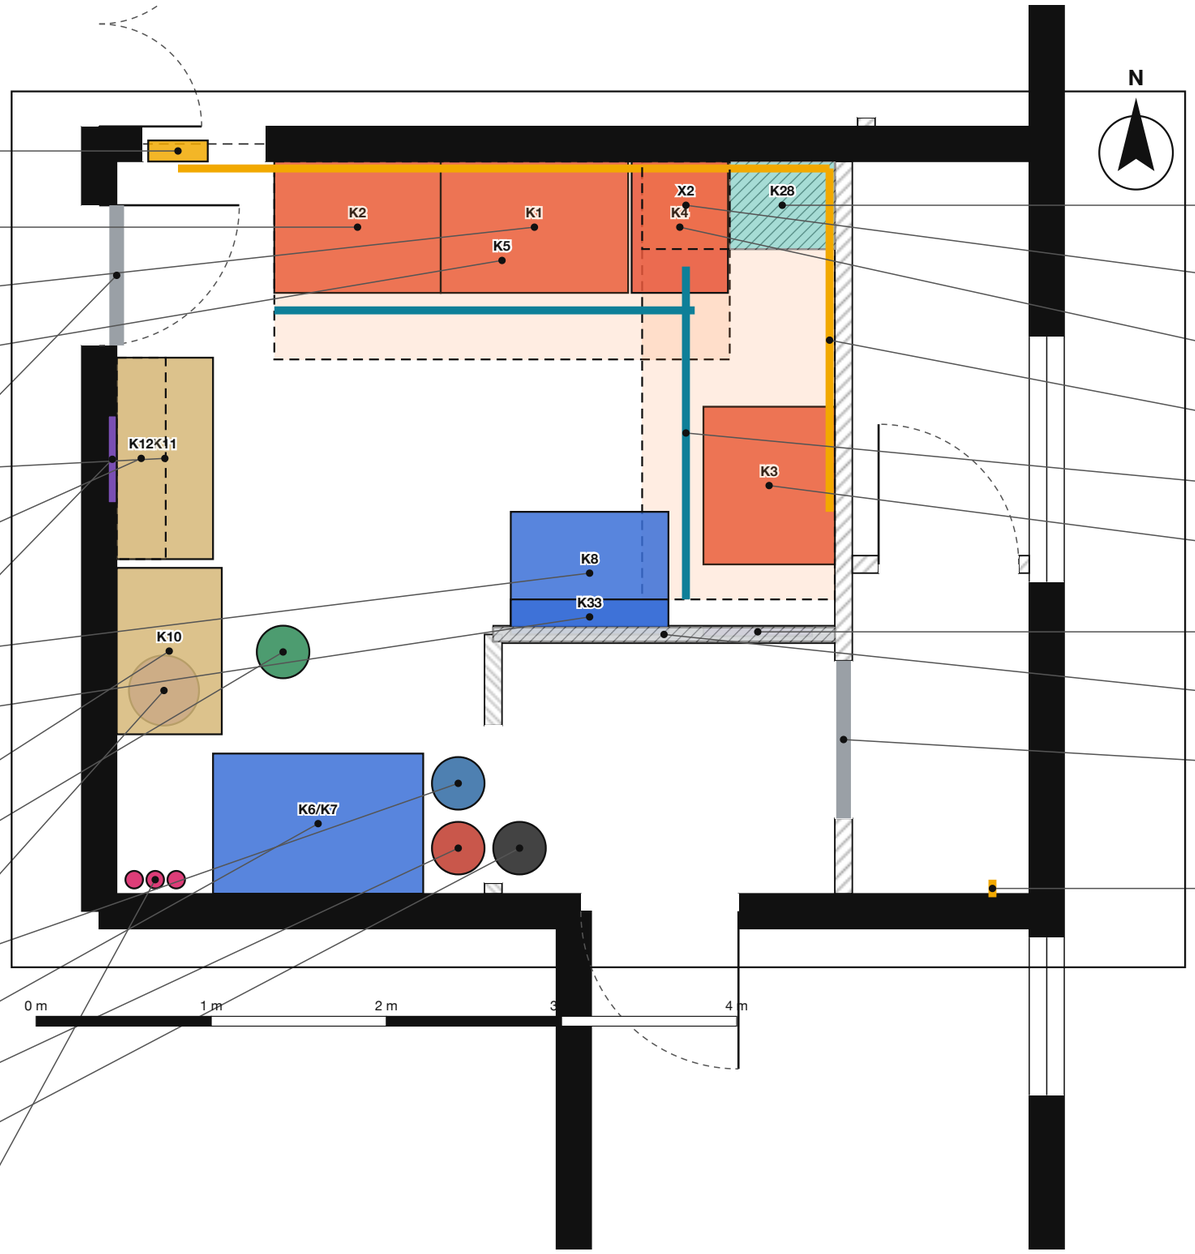



**K29 Gas shut-off + detector**
0.30 × 0.12 × 0.30

**K2 Stock / pot range, 2 burners**
0.95 × 0.75 × 0.80

**K1 Wok range, 2 burners**
1.07 × 0.75 × 0.85

**K5 Exhaust hood**
2.60 × 1.13 × 0.50

**K30 Kitchen door 0.80 m, steel, self-closing**
0.80 × 0.05 × 2.05

**K11 Pass table, by the door**
0.55 × 1.15 × 0.92

**K12 Wall shelf, one tier**
0.30 × 1.15 × 0.04

**K27 KDS screen S2, 21.5 in**
0.50 × 0.05 × 0.29

**K8 Under-counter chiller + raw bench**
0.90 × 0.70 × 0.90

**K33 Chilled prep rail**
0.90 × 0.20 × 0.16

**K10 Veg prep bench**
0.60 × 0.95 × 0.90

**K19d Dustbin, green: veg waste (under K10)**
0.35 × 0.35 × 0.55

**K14 Rice cooker, 10 L**
0.45 × 0.45 × 0.45

**K19c Dustbin, blue: recycling**
0.35 × 0.35 × 0.55

**K6/K7 Dual-zone upright: chiller + freezer**
1.20 × 0.80 × 1.95

**K19a Dustbin, red: non-veg waste**
0.35 × 0.35 × 0.55

**K19b Dustbin, black: dry waste**
0.35 × 0.35 × 0.55

**K20 Fire extinguishers ×3 and fire blanket**
0.15 × 0.15 × 0.50 each

**K28 Sink (existing, NE corner) (existing)**
0.60 × 0.50 × 0.85

**X2 Single duct for the whole L-shaped hood: across the dish wash to the roof exit (X3)**
0.50 × 2.00 × 0.40

**K4 Dim sum steamer, 1 station**
0.55 × 0.75 × 0.90

**K29p Gas pipe (brass) along the north and east walls at 1.0 m, branching to every burner**
about 6.5 m run

**Y1 Hot-line floor trough (drain), L-shaped**
4.30 × 0.10 × 0.10

**K3 Twin-tank fryer, 2 × 15 L**
0.90 × 0.75 × 0.90

**K26 KDS screen S1, 27 in**
0.62 × 0.05 × 0.37

**K31 False partition (existing) (existing)**
1.95 × 0.10 × 2.20

**K32 Washroom opening in the temporary wall (existing)**
0.90 × 0.10 × 2.05

**LPG Gas cylinder bank (4 × 19 kg): outside the east wall of the STORE ROOM, between its two windows, in caged plinth (see sheets A-01 and A-06). Gas pipe runs from there to K29**
0.90 × 0.90 × 0.90 cage, 4 cylinders 0.31 Ø × 0.80

Gas: cooking appliances
Gas: pipe, shut-off valve, cylinders
Refrigeration (chillers, freezers)
Water: sinks, tank, heater, drain grating
Tables, benches, shelves, racks and cabinets
Dustbins (own colour)
Electrics: screens, POS, small appliances
Safety: extinguishers
Exhaust hood and duct (overhead)
Floor drain trough
Structure and openings: doors, hatch, partition, pillar


PROJECT
**Cabin East Garden, Goa** · kitchen block, dish wash, bar, store room

DRAWING
# Kitchen: colour-coded equipment
Every item by type, with its name and size (W × D × H, metres). Gas appliances red, gas pipe and cylinders amber, bins in their own colours

| SCALE AT A3 | SHEET | DATE | REVISION |
|---|---|---|---|
| **1:35** | **E-01** | 3 Nov 2026 | P1 draft |

| STATUS | BASIS |
|---|---|
| **PRELIMINARY, for review** | Client site sketches and photos; clear dimensions in metres |

Not for construction. Sizes marked as assumed are not measured: confirm on site before ordering or building.

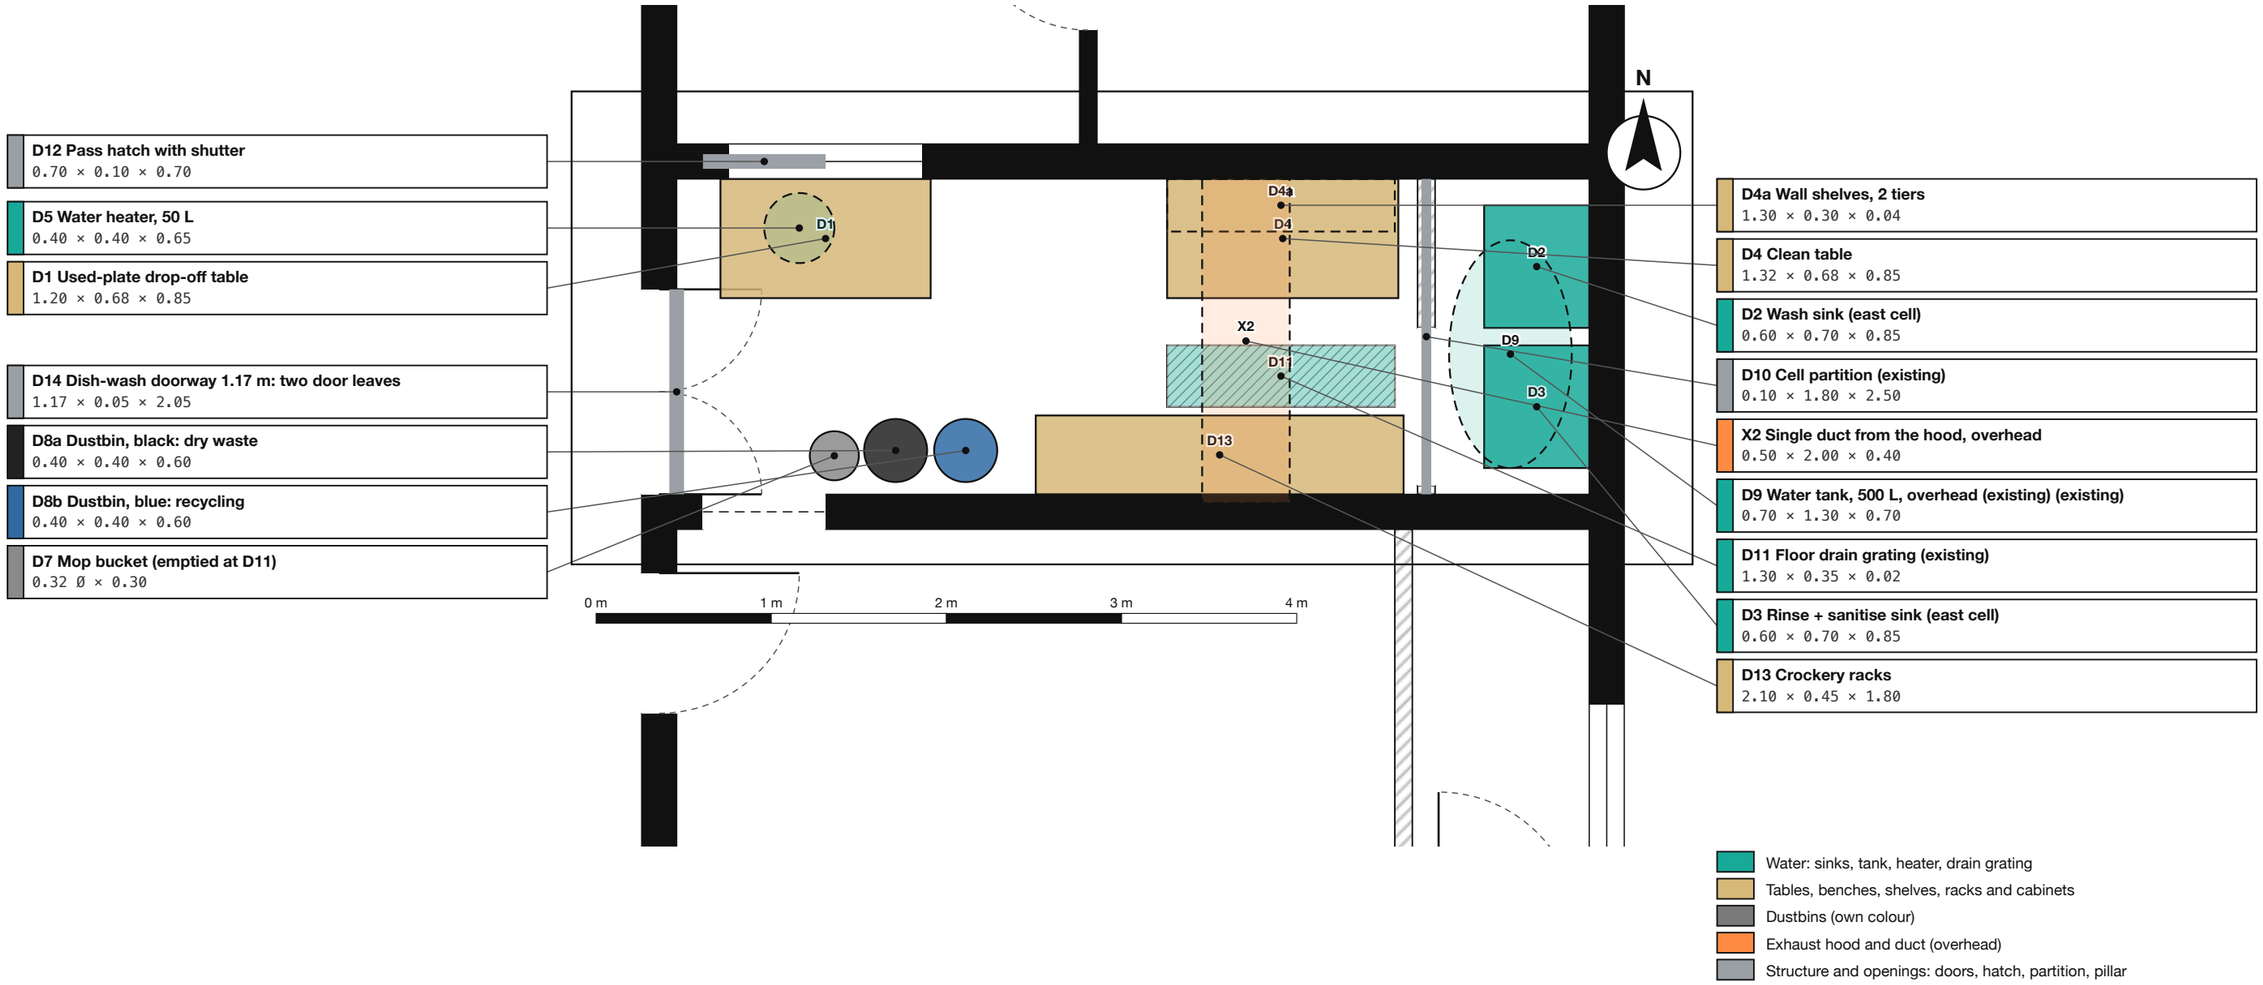



PROJECT
**Cabin East Garden, Goa** · kitchen block, dish wash, bar, store room

DRAWING
# Dish wash: colour-coded equipment
Drop-off table, clean table, crockery racks, the two-sink cell with the 500 L tank above

| SCALE AT A3 | SHEET | DATE | REVISION |
|---|---|---|---|
| **1:35** | **E-02** | 3 Nov 2026 | P1 draft |

| STATUS | BASIS |
|---|---|
| **PRELIMINARY, for review** | Client site sketches and photos; clear dimensions in metres |

Not for construction. Sizes marked as assumed are not measured: confirm on site before ordering or building.

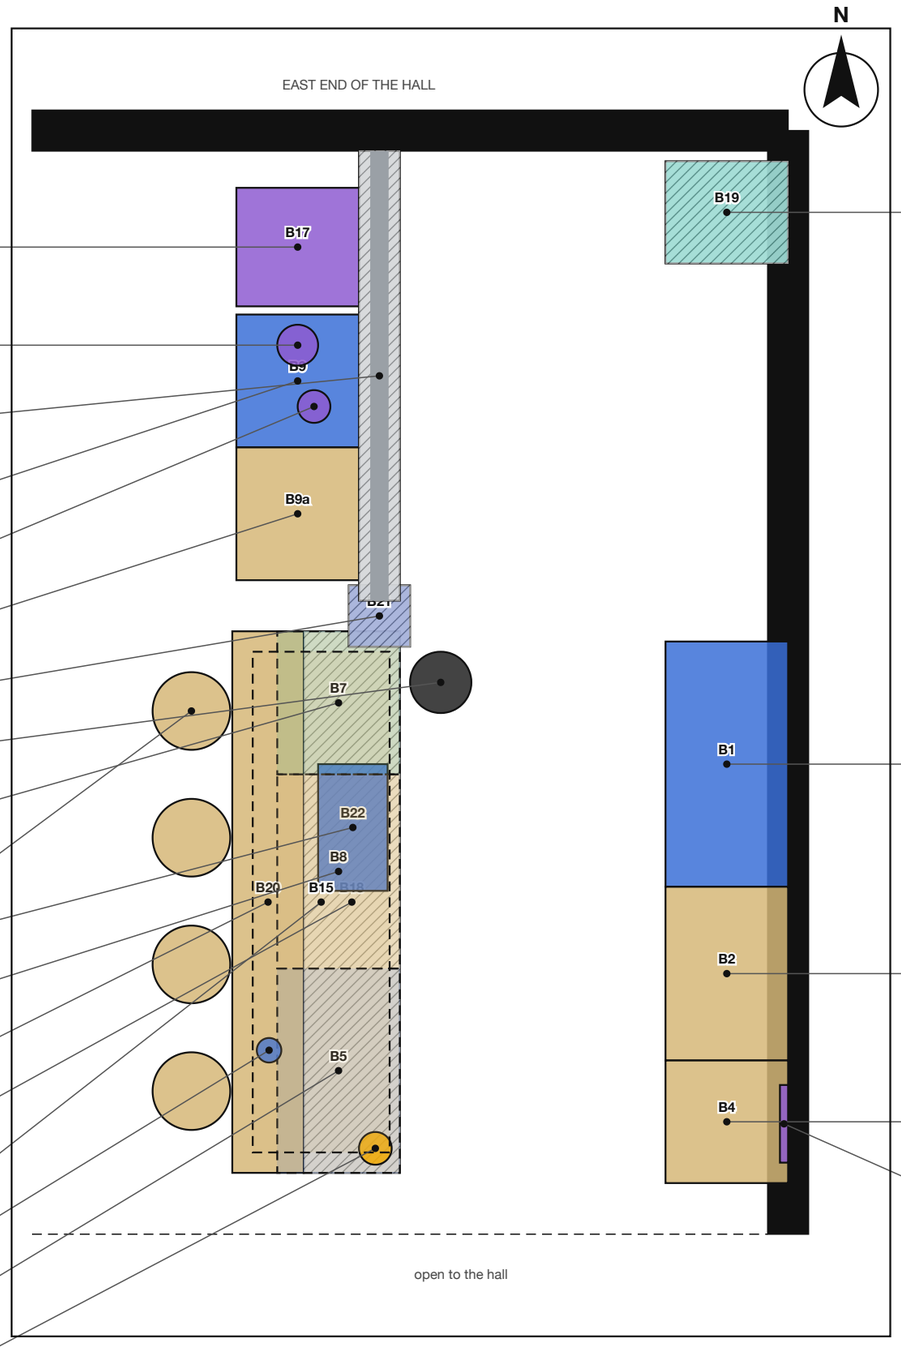


**B17 POS desk**
0.58 × 0.60 × 0.92

**B11 Filter-coffee brewer**
0.45 × 0.40 × 0.65

**CW Coffee wall, brick, 2.20 m long (existing) (existing)**
2.20 × 0.20 × full height

**B9 Under-counter fridge**
0.60 × 0.60 × 0.85

**B12 Hot-water urn**
0.30 × 0.30 × 0.55

**B9a Cupboard under the coffee station (cups, filters)**
0.60 × 0.60 × 0.85

**B21 Blue pillar (existing) (existing)**
0.30 × 0.30 × 3.00

**B14 Bar bin, black: waste**
0.30 × 0.30 × 0.50

**B7 Sink with ice well**
0.70 × 0.55 × 0.85

**ST Bar stools ×4, seat 0.735 m**
0.38 Ø × 0.75

**B22 Chilled garnish rail**
0.34 × 0.62 × 0.16

**B8 Lockable cabinet**
0.95 × 0.60 × 0.85

**B20 Bar top, 1.08 m high**
2.65 × 0.35 × 1.08

**B18 Wooden slab, 0.47 wide (existing) (existing)**
2.65 × 0.47 × 0.92

**B15 Hanging glass rack**
2.60 × 0.67 × 0.28

**B6 Tap font, 3 taps**
0.60 × 0.20 × 0.45

**B5 Keg chiller, 3 kegs**
1.00 × 0.60 × 0.85

**$CO_2$ Gas cylinder ($CO_2$) for the kegs, 2–3 kg, chained beside the keg chiller**
0.15 Ø × 0.50

**B19 Sink in the aisle (existing) (existing)**
0.60 × 0.50 × 0.85

**B1 Bottle cooler, 2 glass doors**
1.20 × 0.60 × 0.85

**B2 Base cabinet (plain)**
0.85 × 0.60 × 0.85

**B4 Back-bar cabinet**
0.60 × 0.60 × 0.85

**B16 KDS screen S3, 15.6 in**
0.38 × 0.03 × 0.23

0 m 1 m 2 m 3 m 4 m

- Refrigeration (chillers, freezers)
- Water: sinks, tank, heater, drain grating
- Tables, benches, shelves, racks and cabinets
- Electrics: screens, POS, small appliances
- Gas: pipe, shut-off valve, cylinders
- Dustbins (own colour)
- Structure and openings: doors, hatch, partition, pillar

PROJECT
**Cabin East Garden, Goa** · kitchen block, dish wash, bar, store room

DRAWING
# Bar: colour-coded equipment
Counter with the raised bar top over the work slab, coffee station on the coffee wall, keg chiller and its $CO_2$ cylinder

| SCALE AT A3 | SHEET | DATE | REVISION |
|---|---|---|---|
| **1:30** | **E-03** | 3 Nov 2026 | P1 draft |

| STATUS | BASIS |
|---|---|
| **PRELIMINARY, for review** | Client site sketches and photos; clear dimensions in metres |

Not for construction. Sizes marked as assumed are not measured: confirm on site before ordering or building.