
CABIN EAST GARDEN · EQUIPMENT PLAN

1 · Kitchen

5.41 × 4.38 m wall to wall · 5.21 × 4.18 m clear · Equipment floor area 8.5 m² of 21.8 m² (39%)

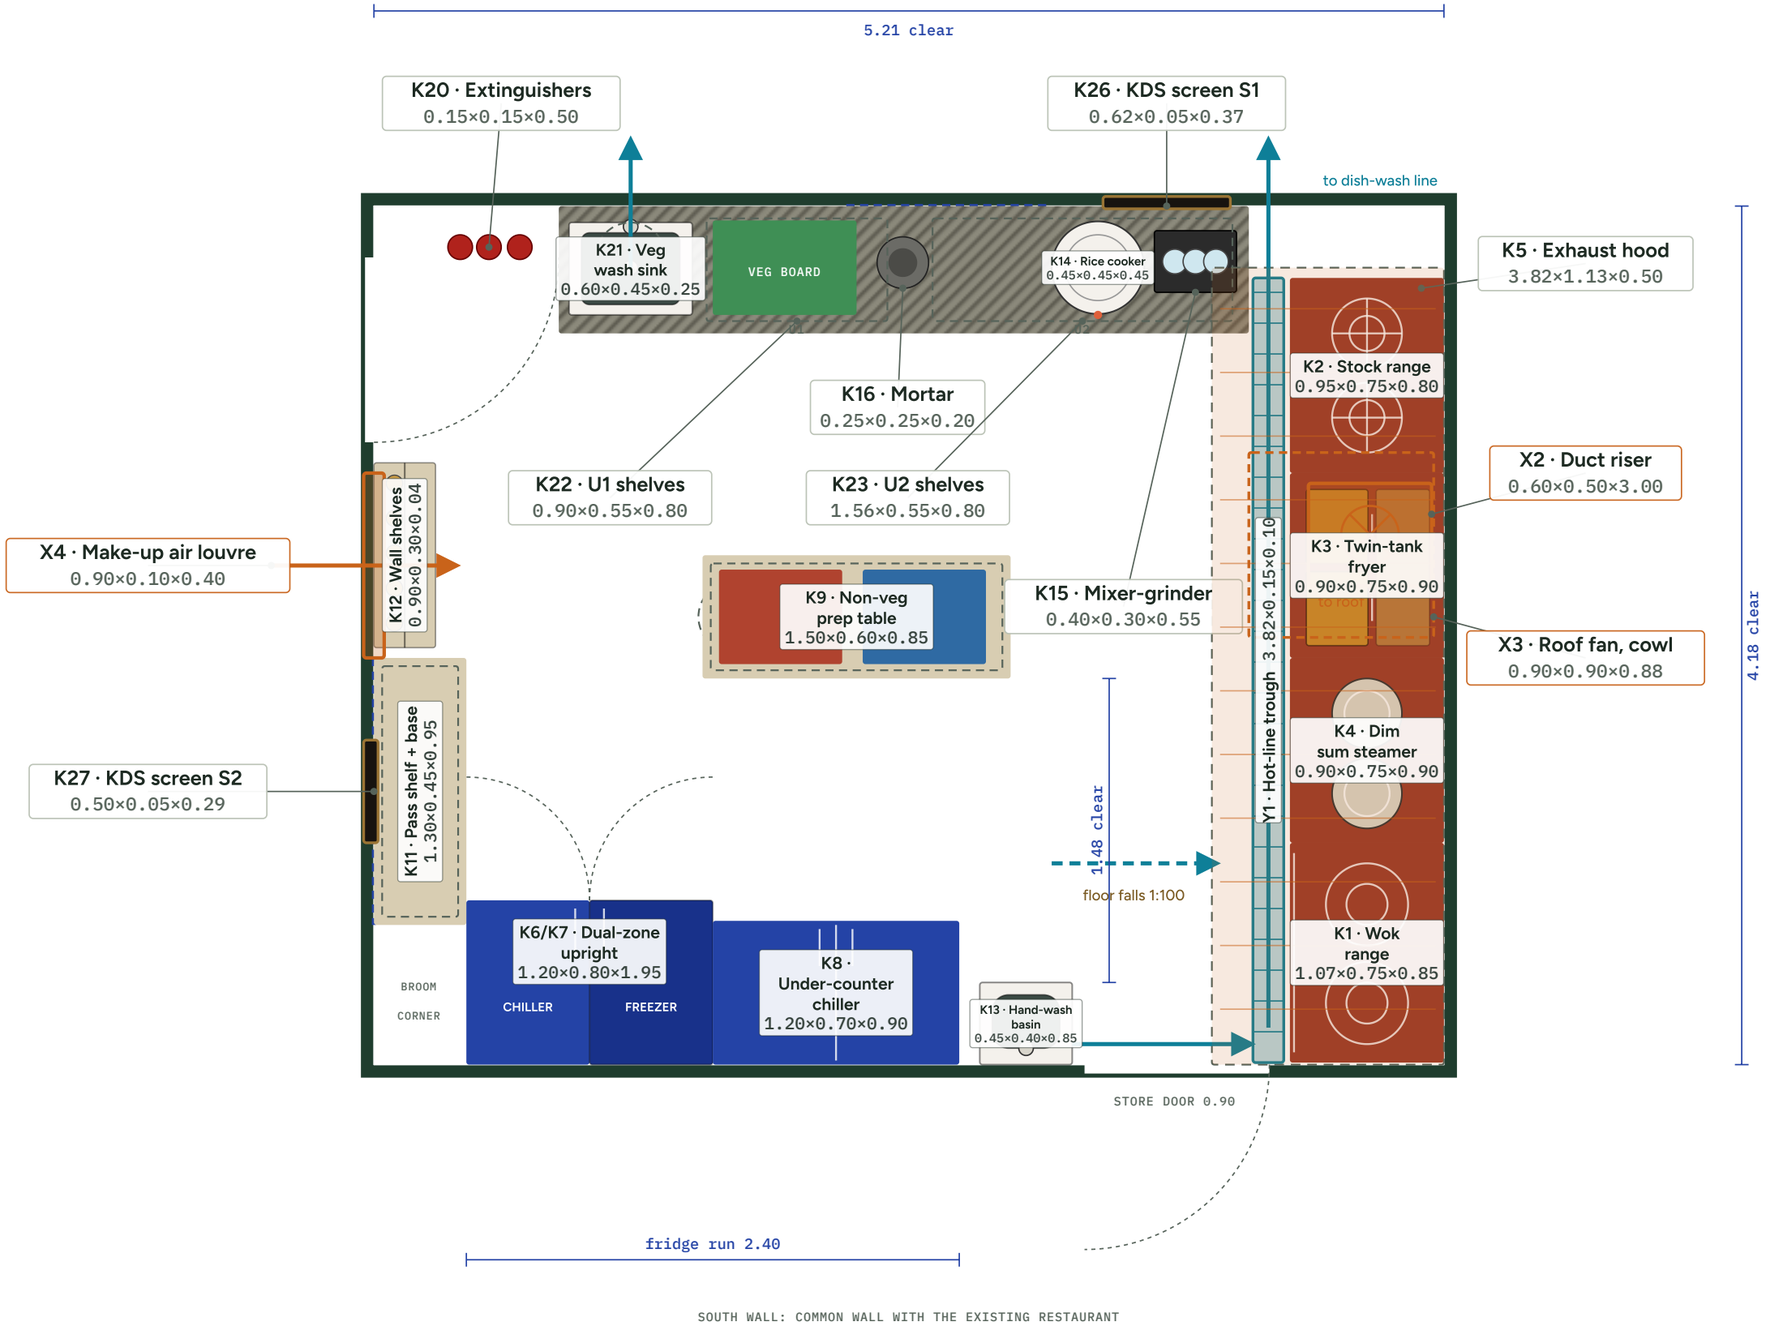

COLOUR CODE

Hot (gas) cooking #9A3B2A · Refrigerated #2443A6 · Freezer #18318A · Wet / wash #2D6B4D · Tables, shelves, racks, cabinets #D8CDB2 · Sits on a bench or counter #C79A45 · Already built (hatched)


Above or in the floor (dashed outline) · Exhaust and air #C9631A · Drainage #0E7F98 · Wall #1F3D2E · Window · Door swing · Dirty to clean flow · Kitchen screens (KDS) #17130F

Plan view, north up · Scale about 1:30 at A3 · Each item carries its number, name and size in metres, W × D × H (W along the wall, D out from the wall, H floor to top) · Items too small to hold their label have a leader callout beside them · Sizes are planning figures to be confirmed on site

CABIN EAST GARDEN · EQUIPMENT PLAN

2 · Dish wash

5.41 × 2.00 m wall to wall · 5.21 × 1.80 m clear · Equipment floor area 3.7 m² of 9.4 m² (39%)

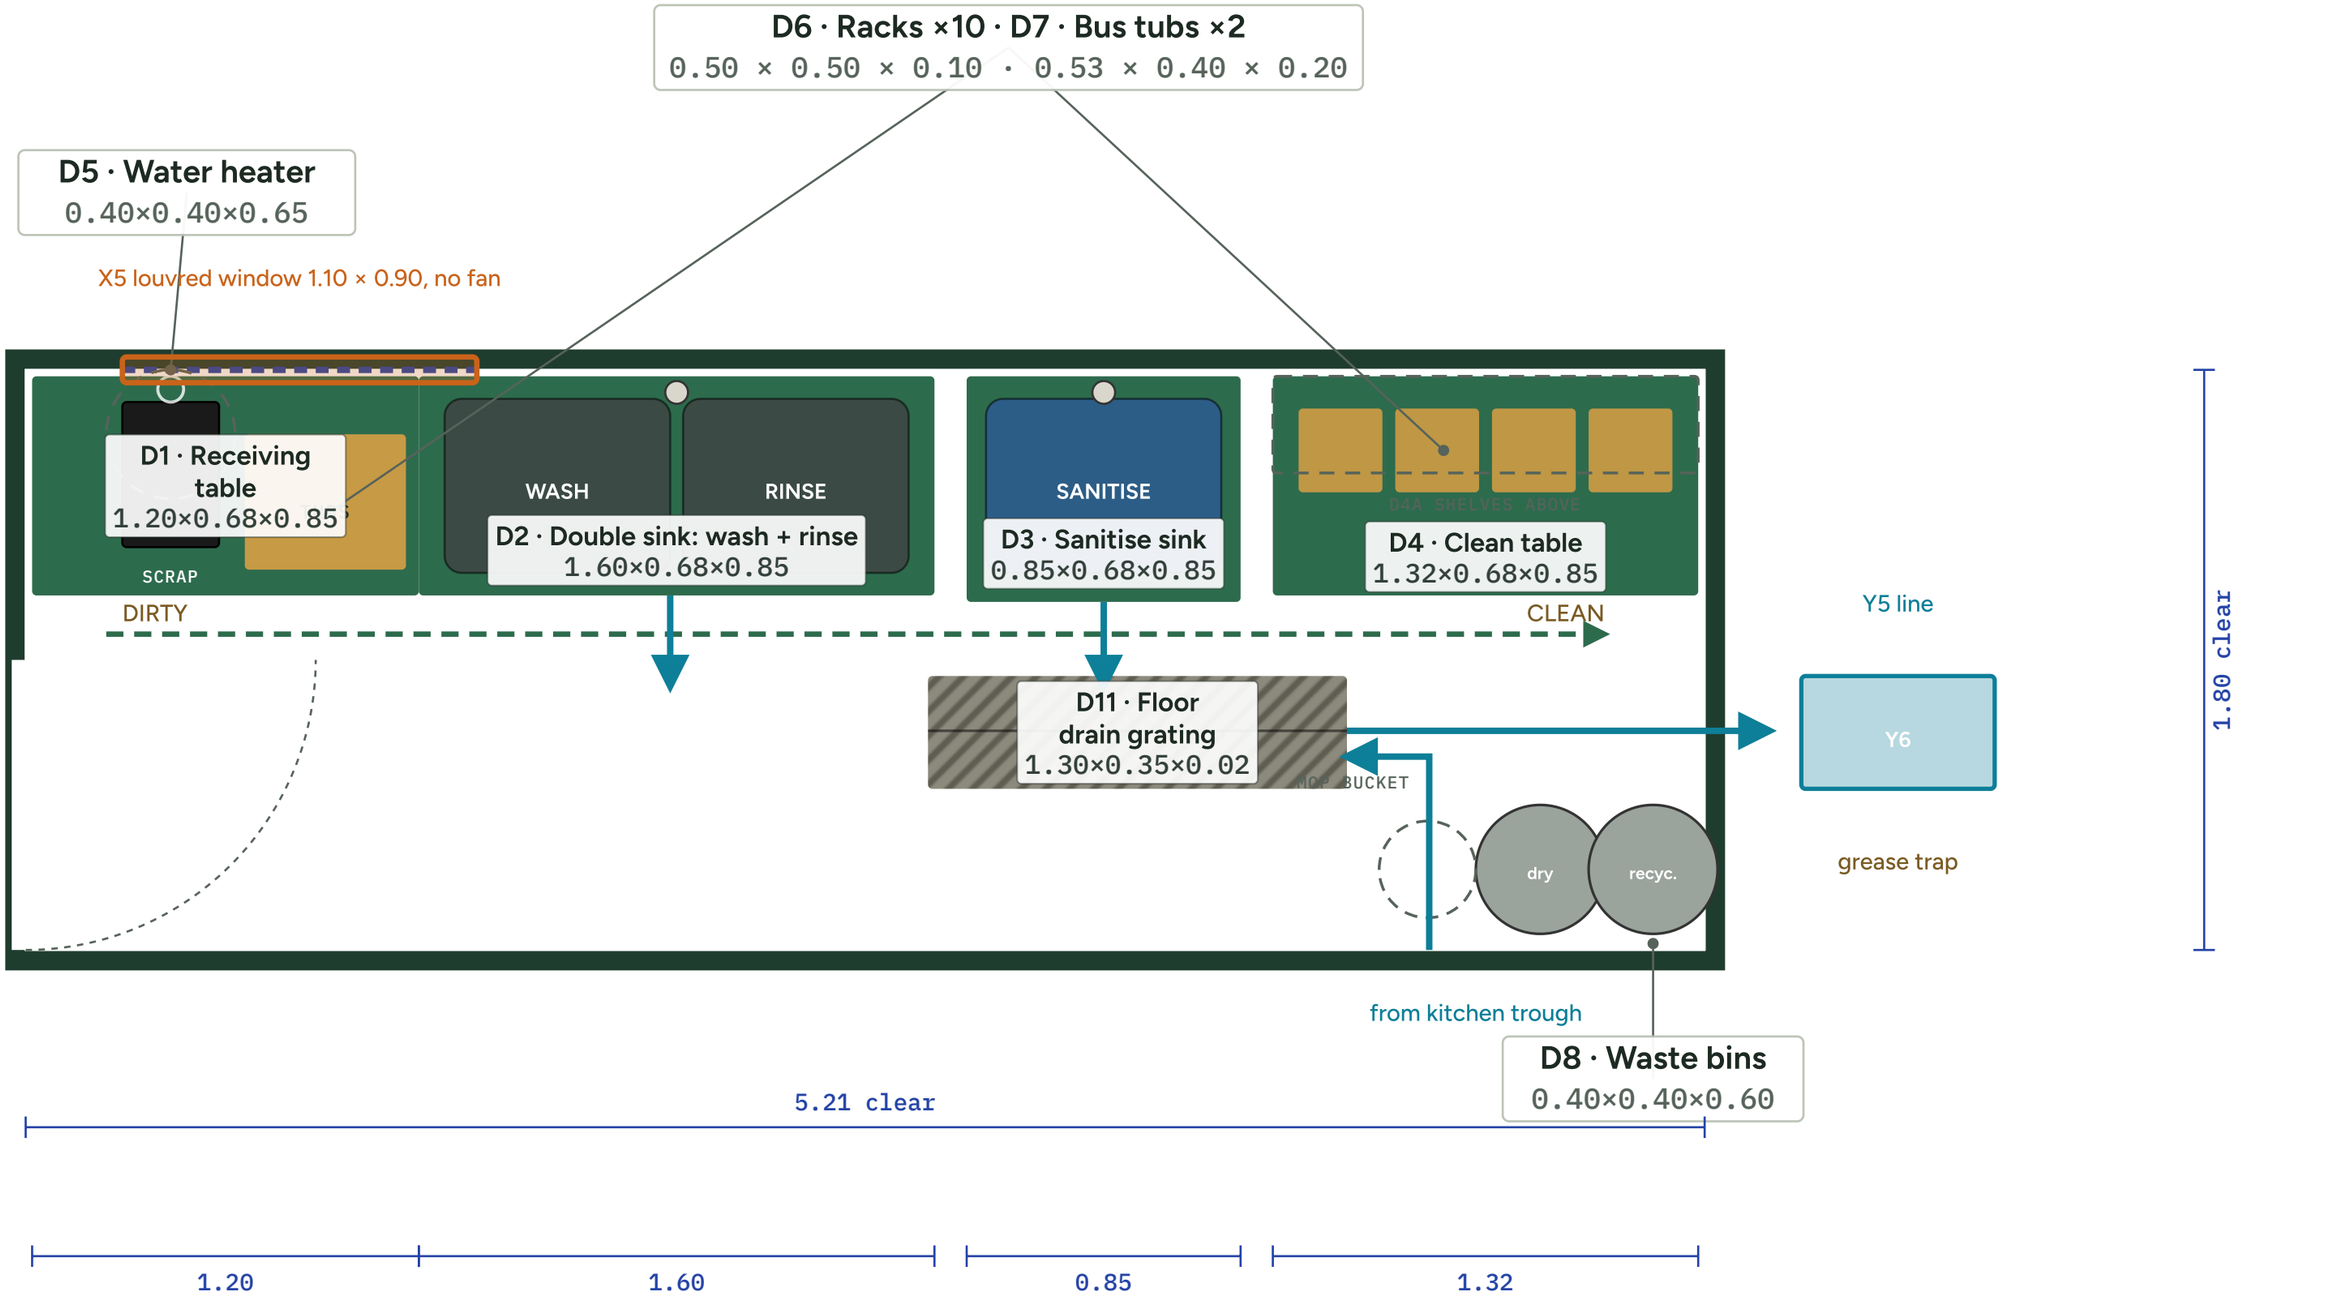


COLOUR CODE — Hot (gas) cooking #9A3B2A · Refrigerated #2443A6 · Freezer #18318A · Wet / wash #2D6B4D · Tables, shelves, racks, cabinets #D8CDB2 · Sits on a bench or counter #C79A45 · Already built (hatched) · Above or in the floor (dashed outline) · Exhaust and air #C9631A · Drainage #0E7F98 · Wall #1F3D2E · Window · Door swing · Dirty to clean flow · Kitchen screens (KDS) #17130F

Plan view, north up · Scale about 1:19 at A3 · Each item carries its number, name and size in metres, W × D × H (W along the wall, D out from the wall, H floor to top) · Items too small to hold their label have a leader callout beside them · Sizes are planning figures to be confirmed on site

CABIN EAST GARDEN · EQUIPMENT PLAN

3 · Bar

Back bar 2.80 m · counter 2.80 m · coffee station 1.30 m

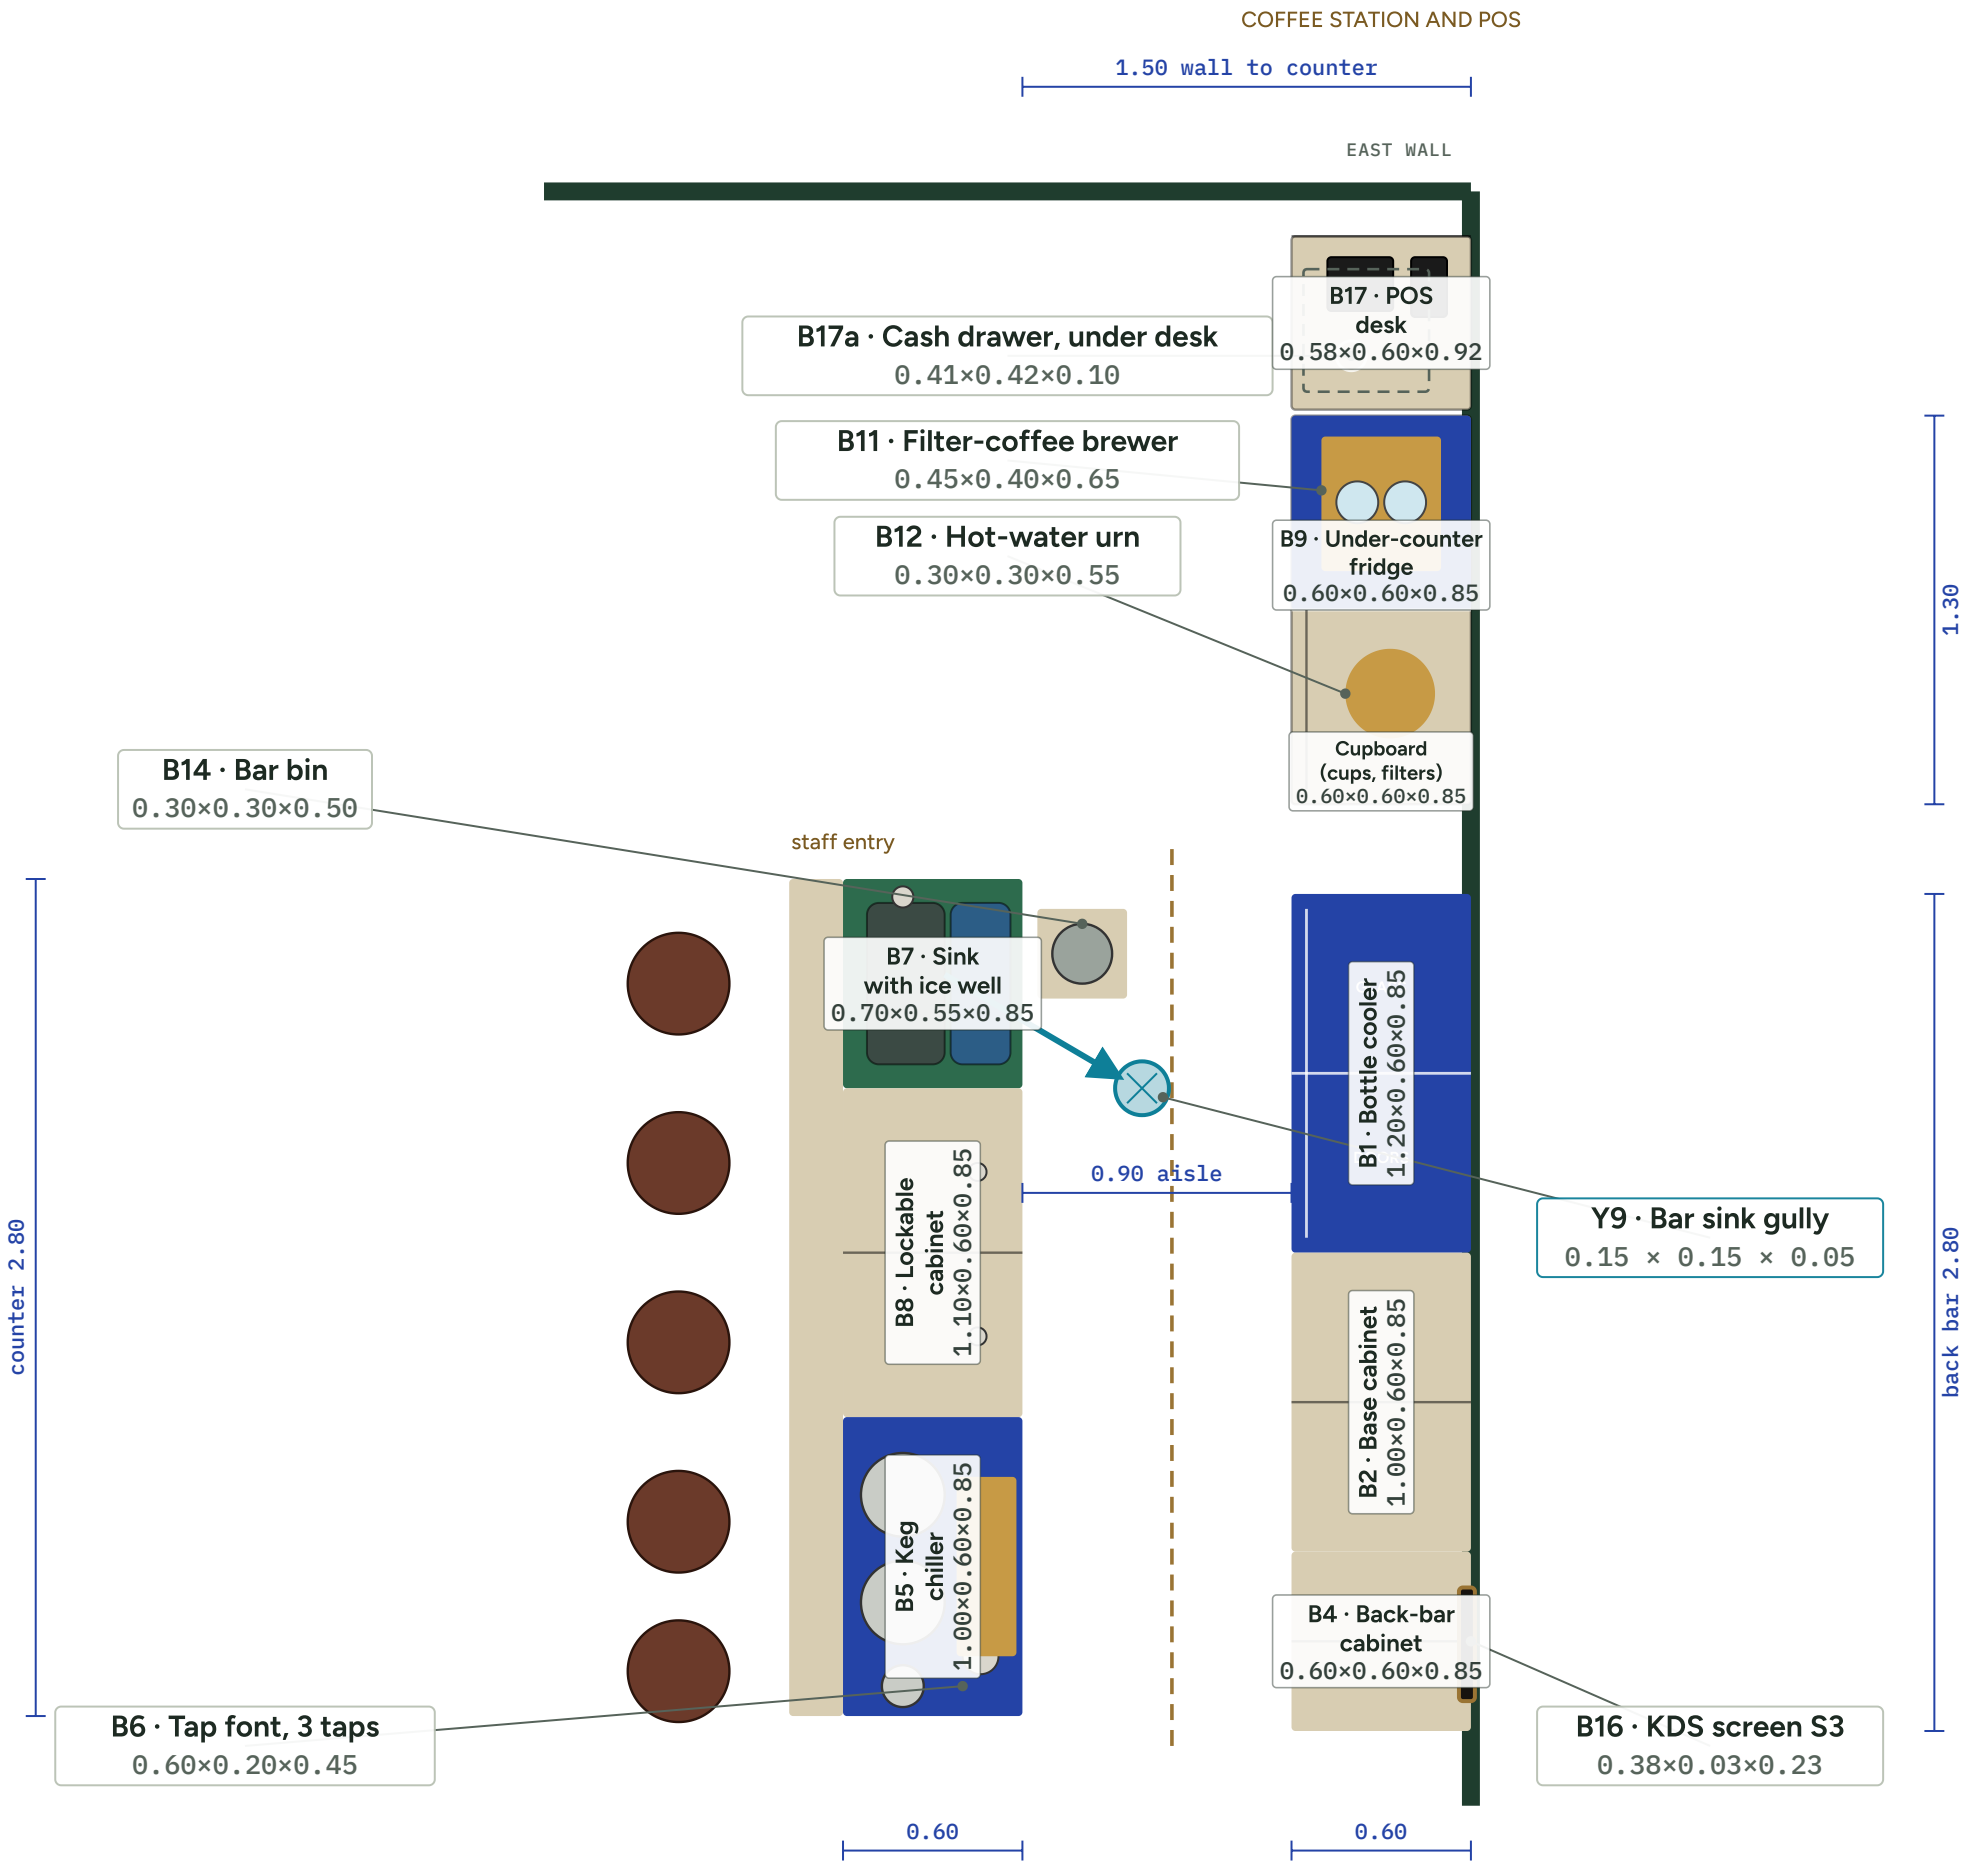

COLOUR CODE

Hot (gas) cooking #9A3B2A · Refrigerated #2443A6 · Freezer #18318A · Wet / wash #2D6B4D · Tables, shelves, racks, cabinets #D8CDB2

Sits on a bench or counter #C79A45 · Already built (hatched) · Above or in the floor (dashed outline) · Exhaust and air #C9631A · Drainage #0E7F98


Wall #1F3D2E · Window · Door swing · Dirty to clean flow · Kitchen screens (KDS) #17130F

Plan view, north up · Scale about 1:25 at A3 · Each item carries its number, name and size in metres, W × D × H (W along the wall, D out from the wall, H floor to top) · Items too small to hold their label have a leader callout beside them · Sizes are planning figures to be confirmed on site

CABIN EAST GARDEN · EQUIPMENT PLAN

4 · Store room

2.70 × 6.46 m wall to wall · 2.50 × 6.26 m clear · door from the kitchen at the north end · Racks and stacks cover 6.3 m² of 15.6 m² (40%)

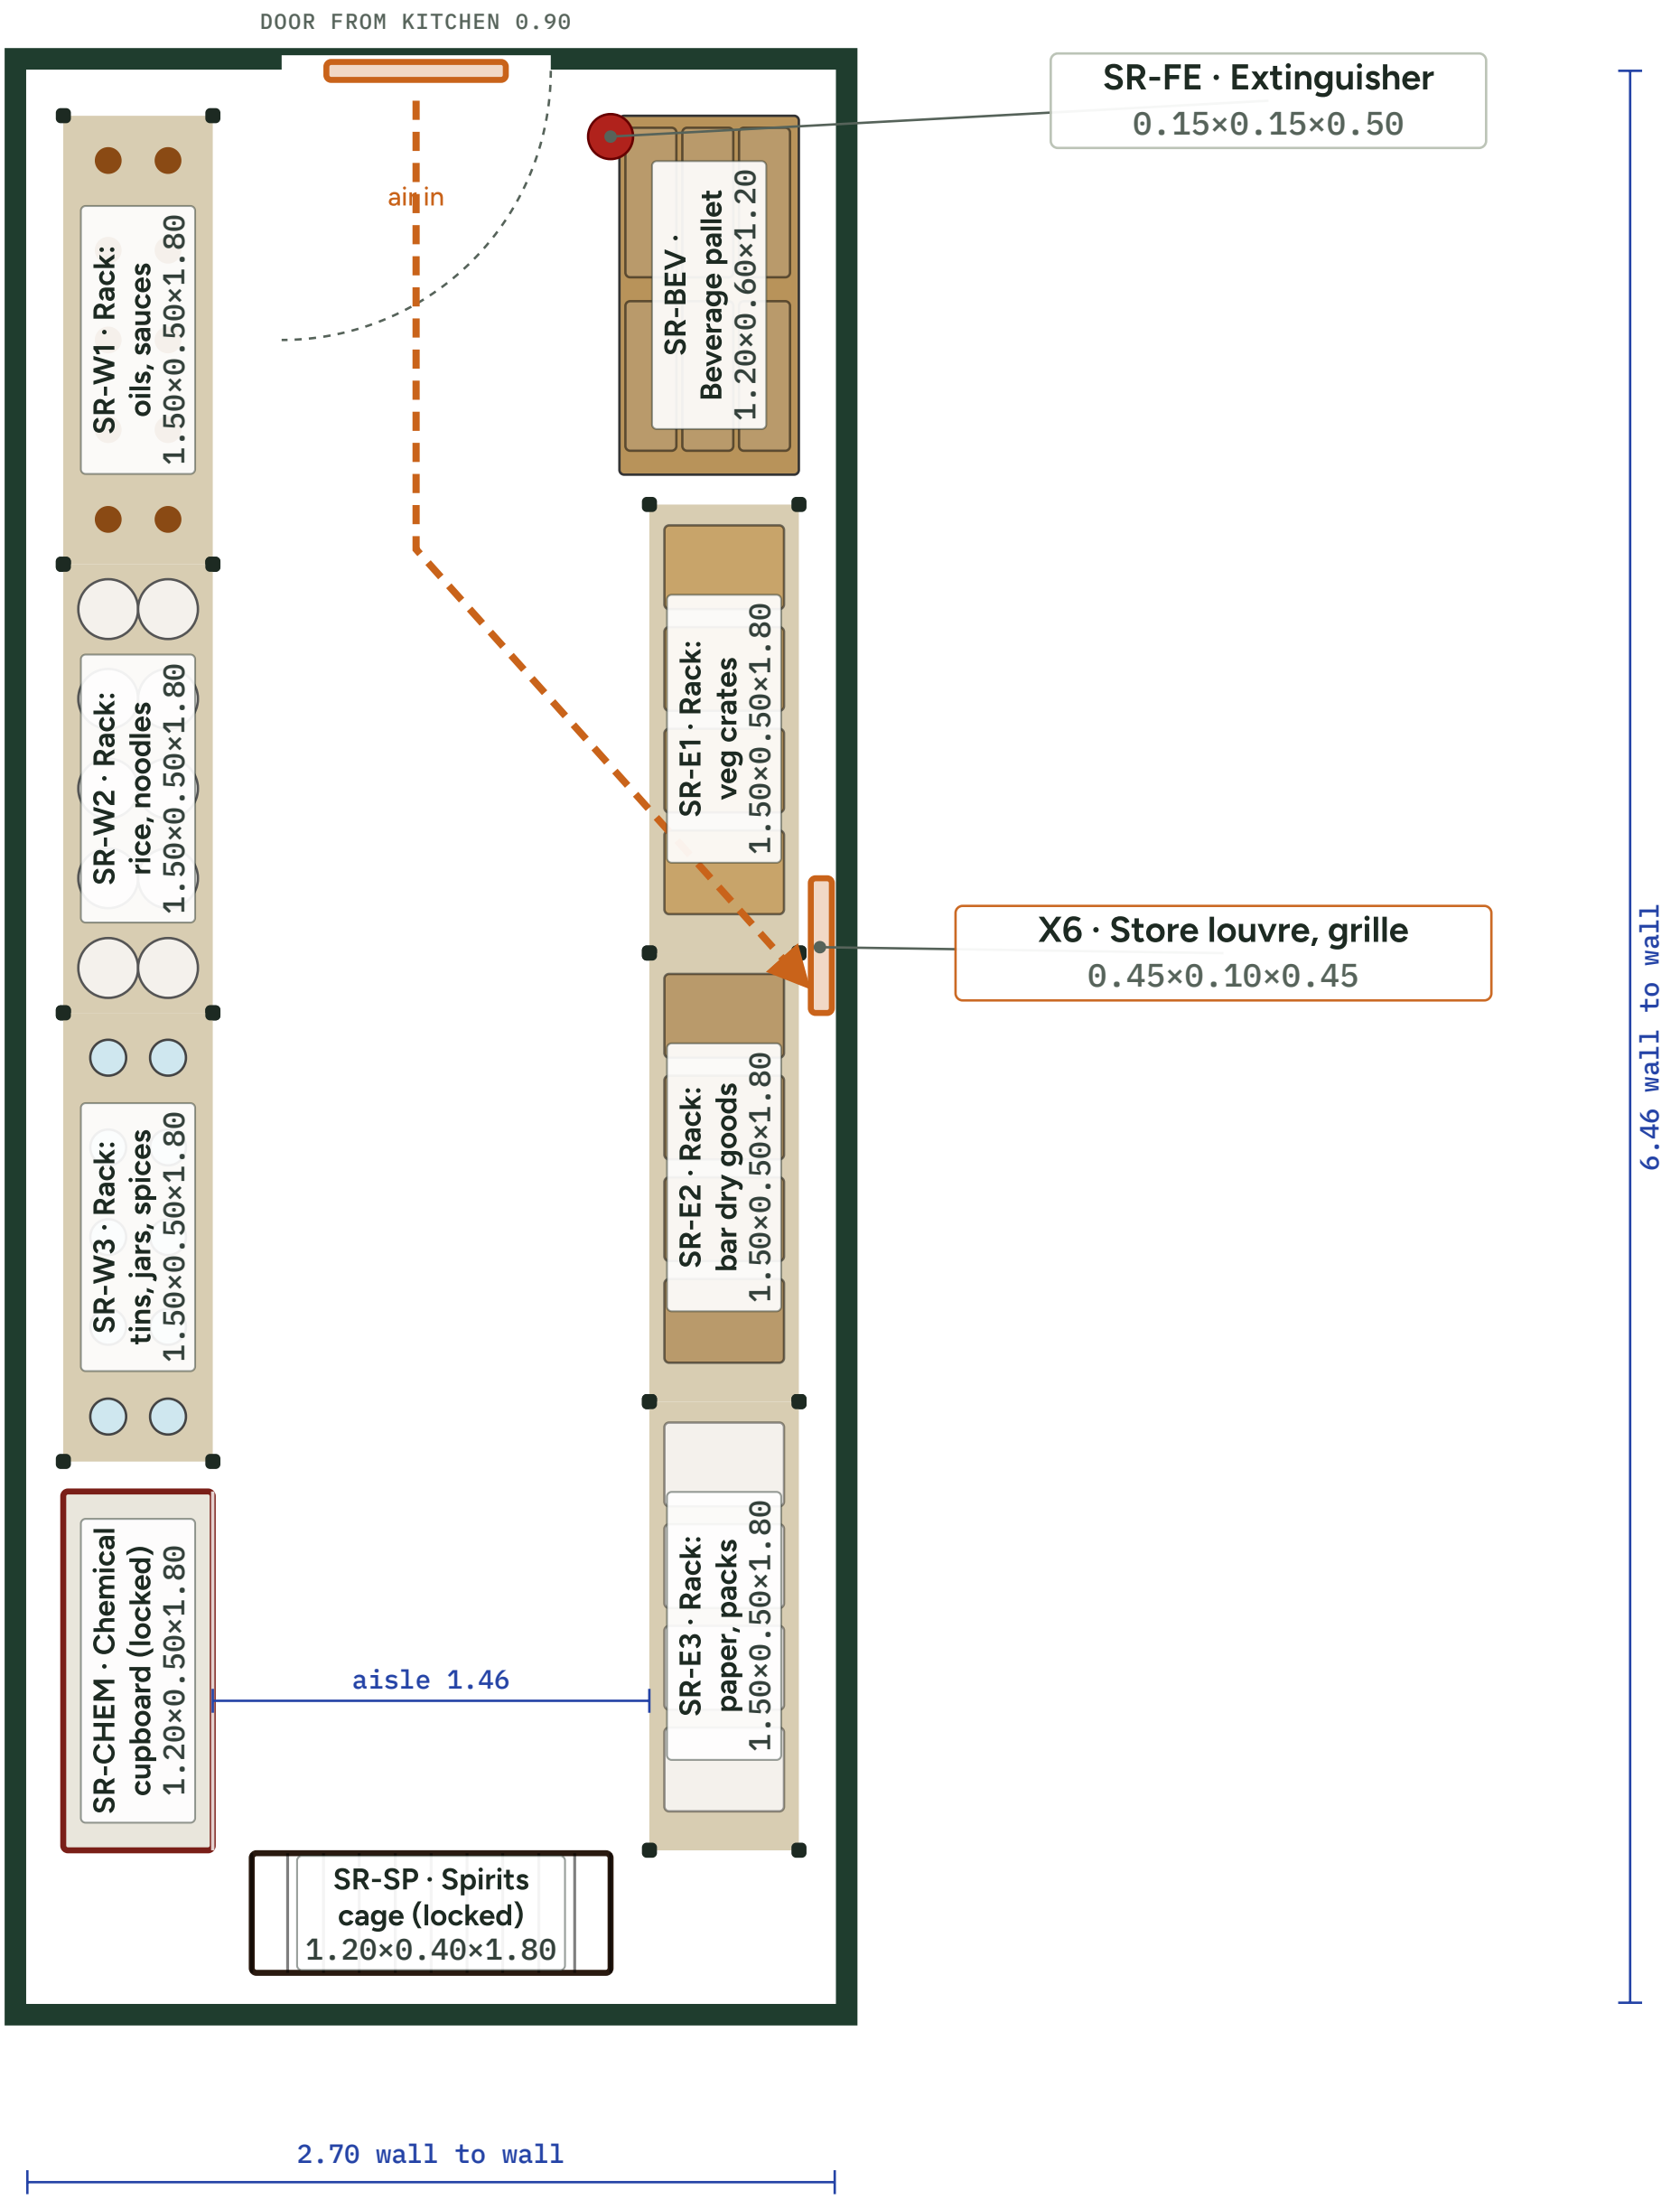

COLOUR CODE

Hot (gas) cooking #9A3B2A · Refrigerated #2443A6 · Freezer #18318A · Wet / wash #2D6B4D · Tables, shelves, racks, cabinets #D8CDB2

Sits on a bench or counter #C79A45 · Already built (hatched) · Above or in the floor (dashed outline) · Exhaust and air #C9631A · Drainage #0E7F98


Wall #1F3D2E · Window · Door swing · Dirty to clean flow · Kitchen screens (KDS) #17130F

Plan view, north up · Scale about 1:23 at A3 · Each item carries its number, name and size in metres, W × D × H (W along the wall, D out from the wall, H floor to top) · Items too small to hold their label have a leader callout beside them · Sizes are planning figures to be confirmed on site

CABIN EAST GARDEN · EQUIPMENT PLAN

5 · Exhaust system

Block plan, north up · hood over the hot line, duct riser and roof fan, make-up air louvre, and the room louvres · sizes W × D × H in metres

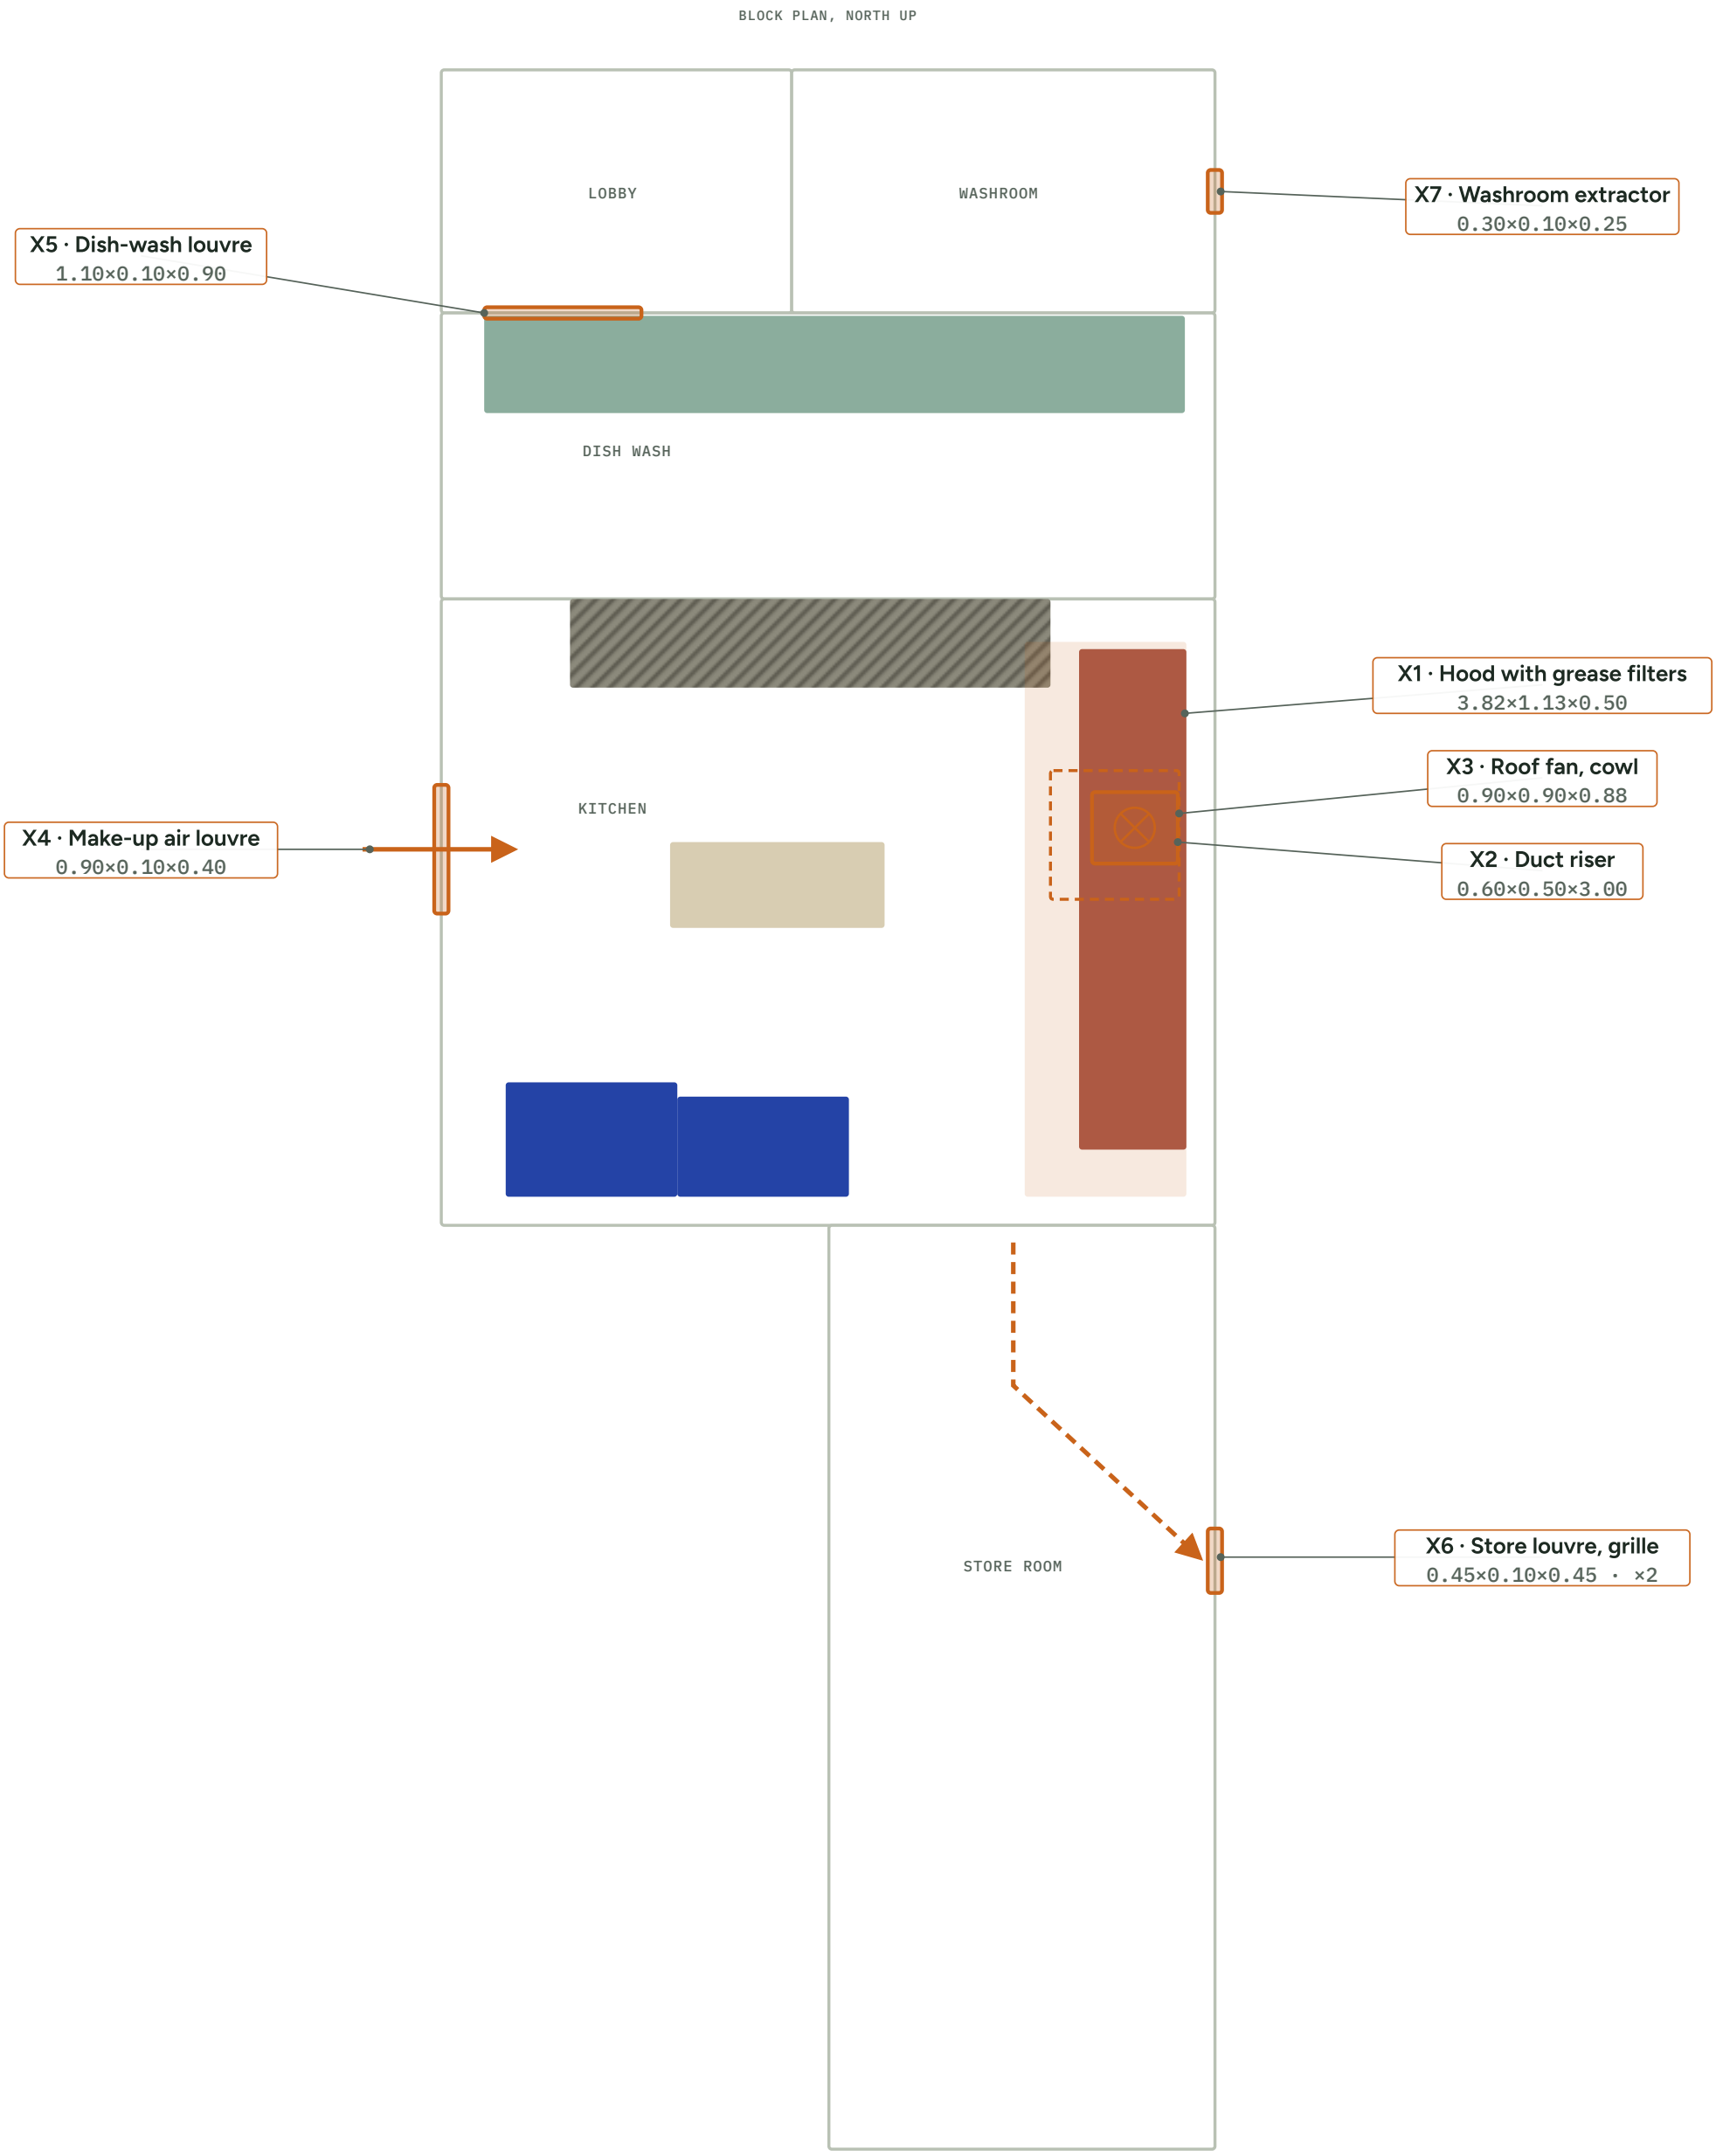

COLOUR CODE

- Hot (gas) cooking #9A3B2A
- Refrigerated #2443A6
- Freezer #18318A
- Wet / wash #2D6B4D
- Tables, shelves, racks, cabinets #D8CDB2
- Sits on a bench or counter #C79A45
- Already built (hatched)
- Above or in the floor (dashed outline)
- Exhaust and air #C9631A
- Drainage #0E7F98
- Wall #1F3D2E
- Window
- Door swing
- Dirty to clean flow
- Kitchen screens (KDS) #17130F

Plan view, north up · Scale about 1:46 at A3 · Each item carries its number, name and size in metres, W × D × H (W along the wall, D out from the wall, H floor to top) · Items too small to hold their label have a leader callout beside them · Sizes are planning figures to be confirmed on site